




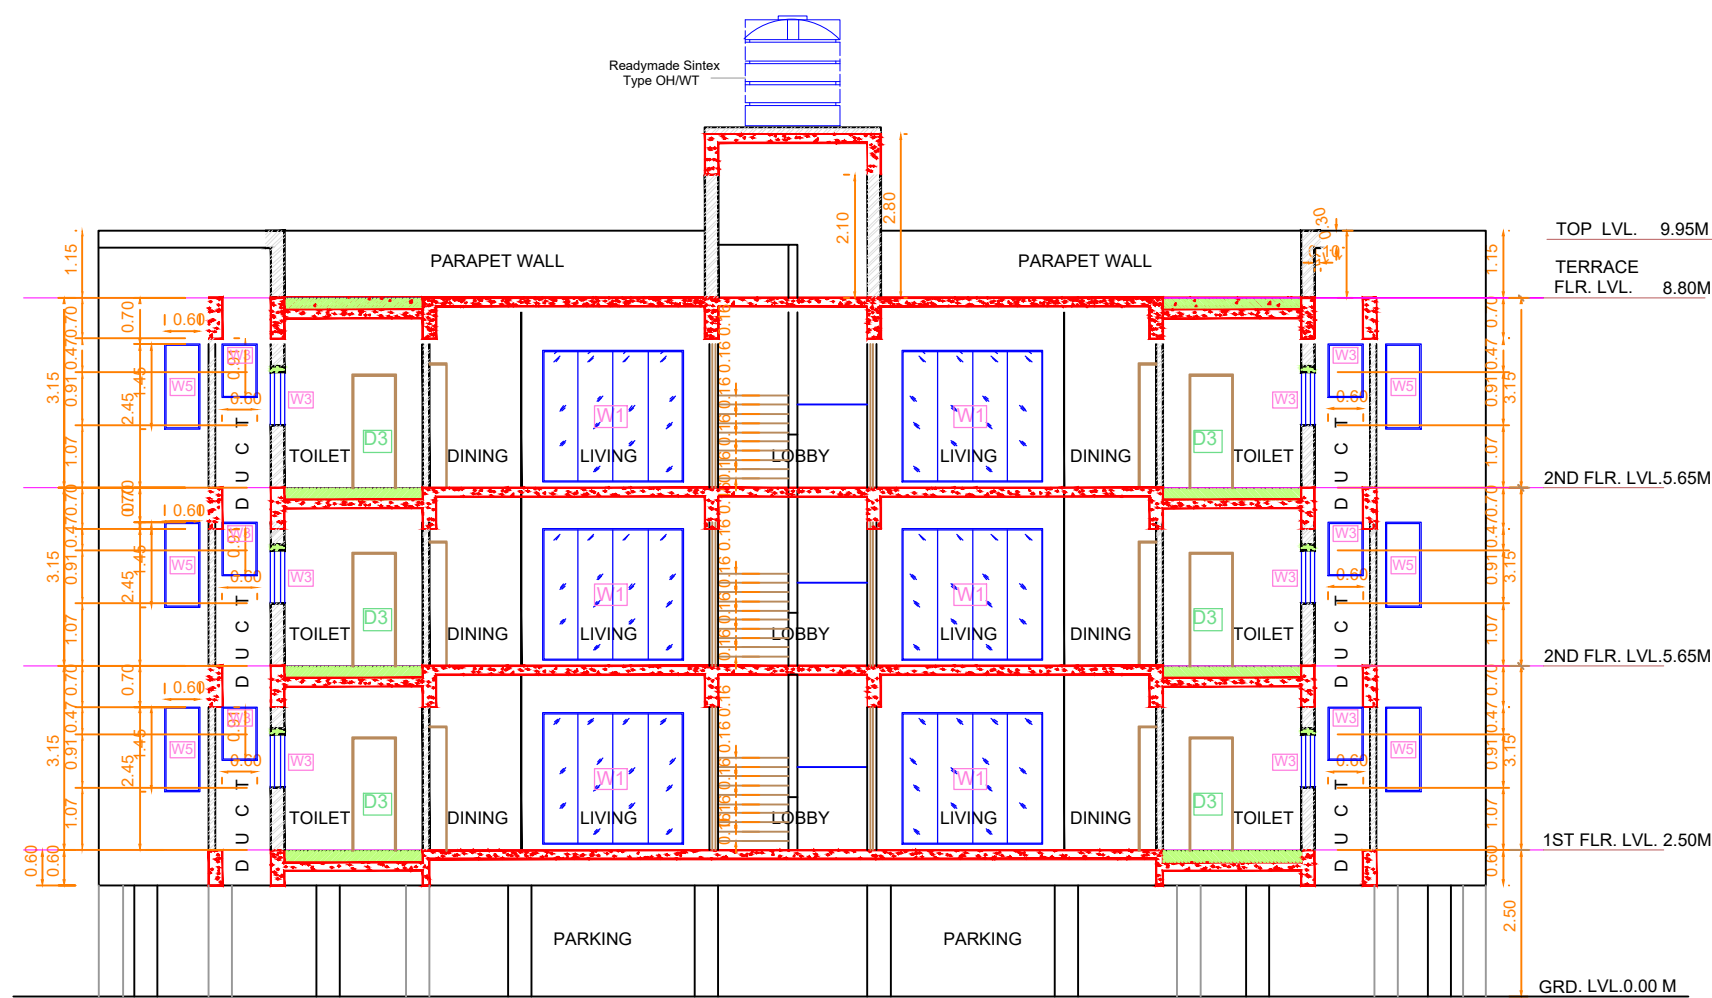


SECTION B-B

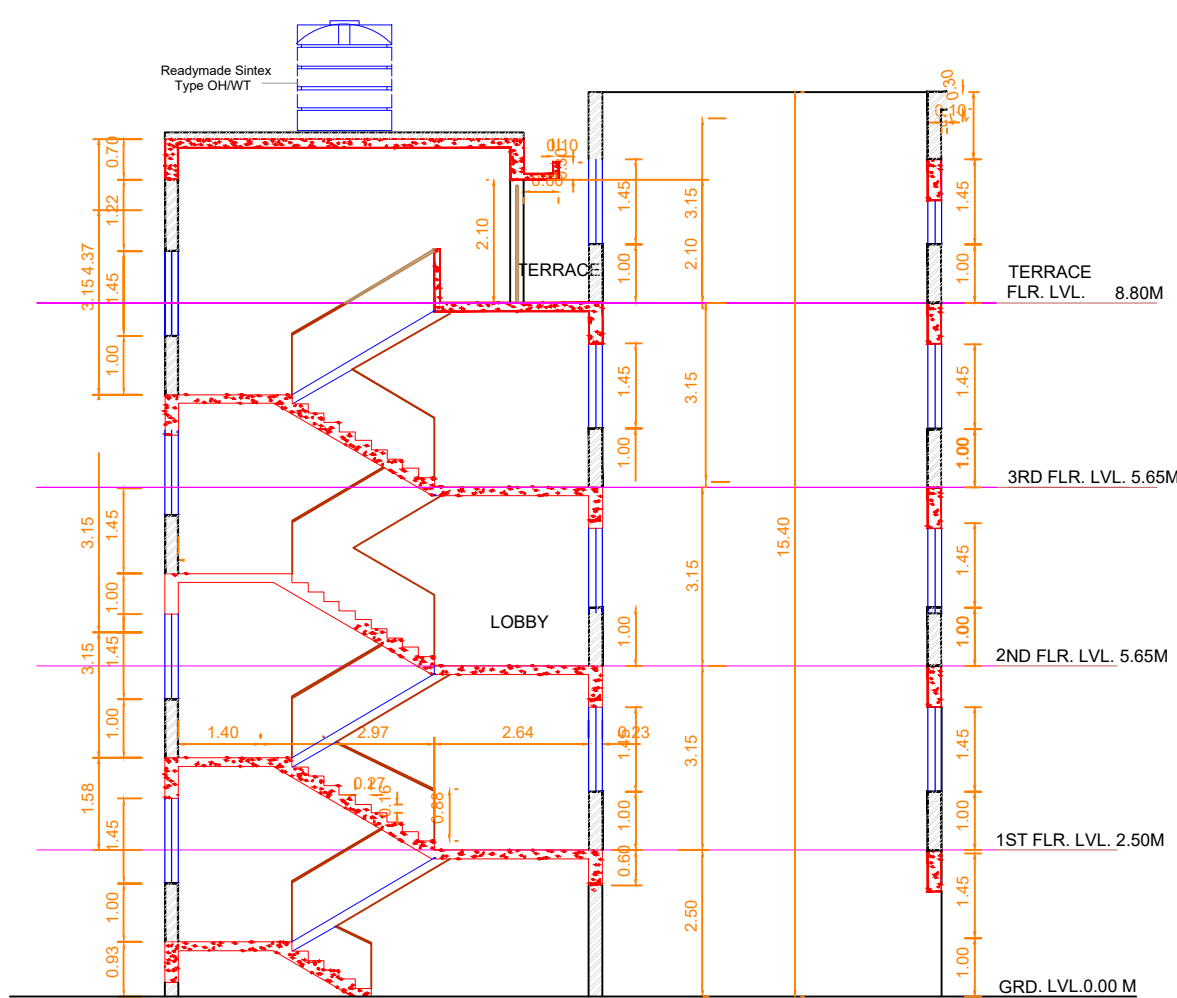


SECTION A-A

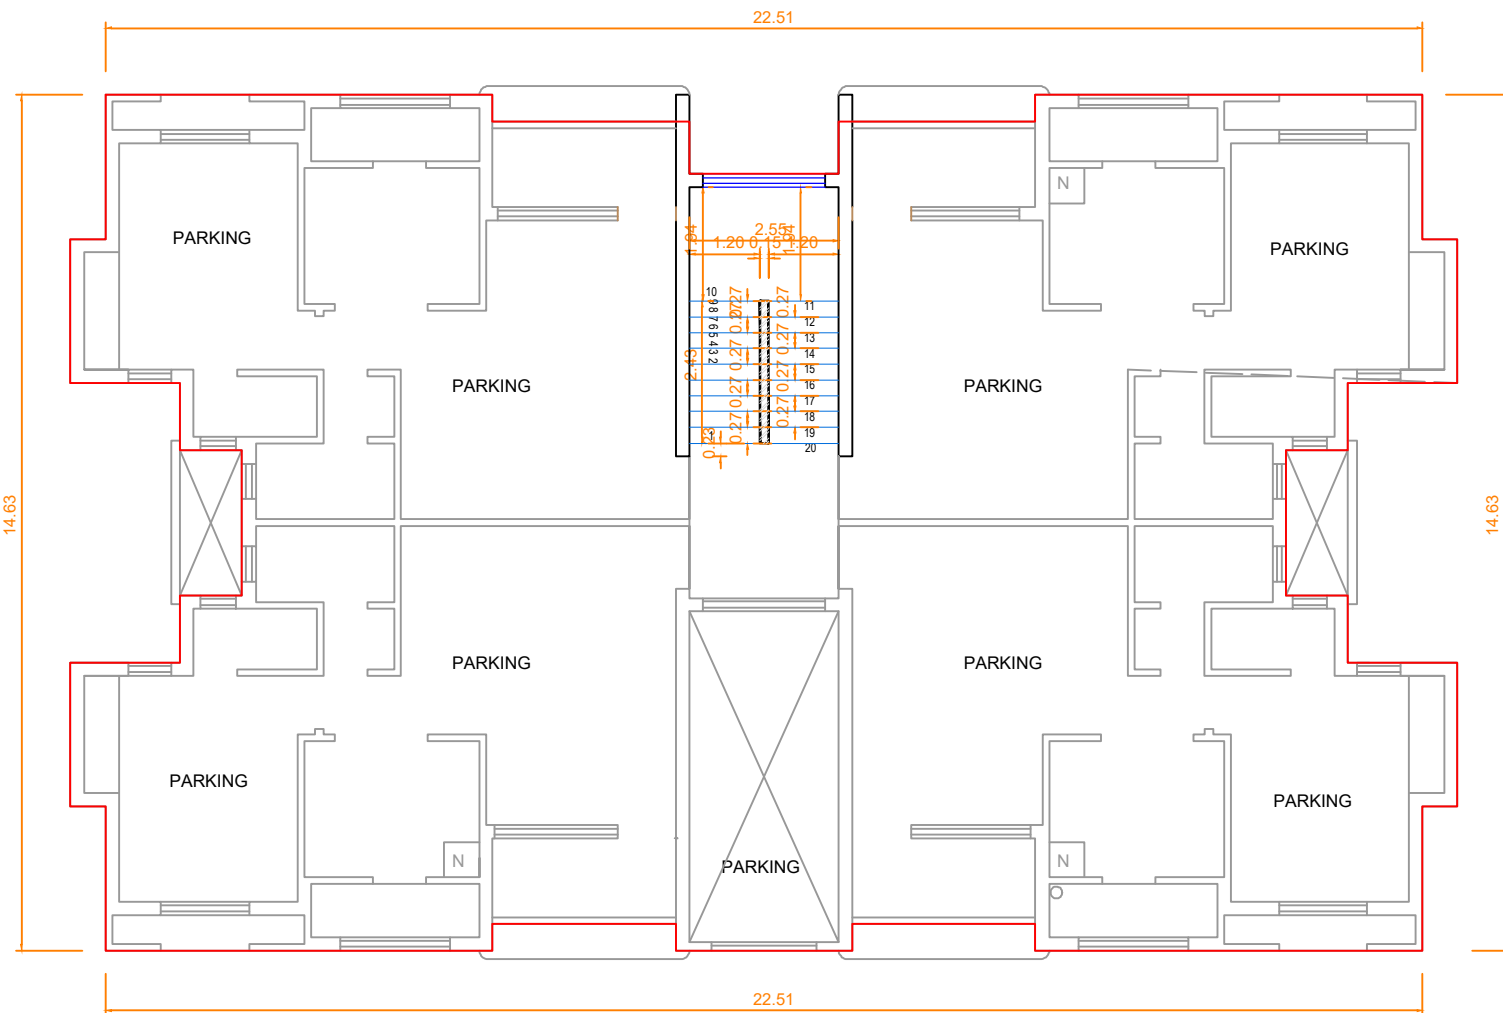

PROPOSED STILT / PARKING FLOOR PLAN

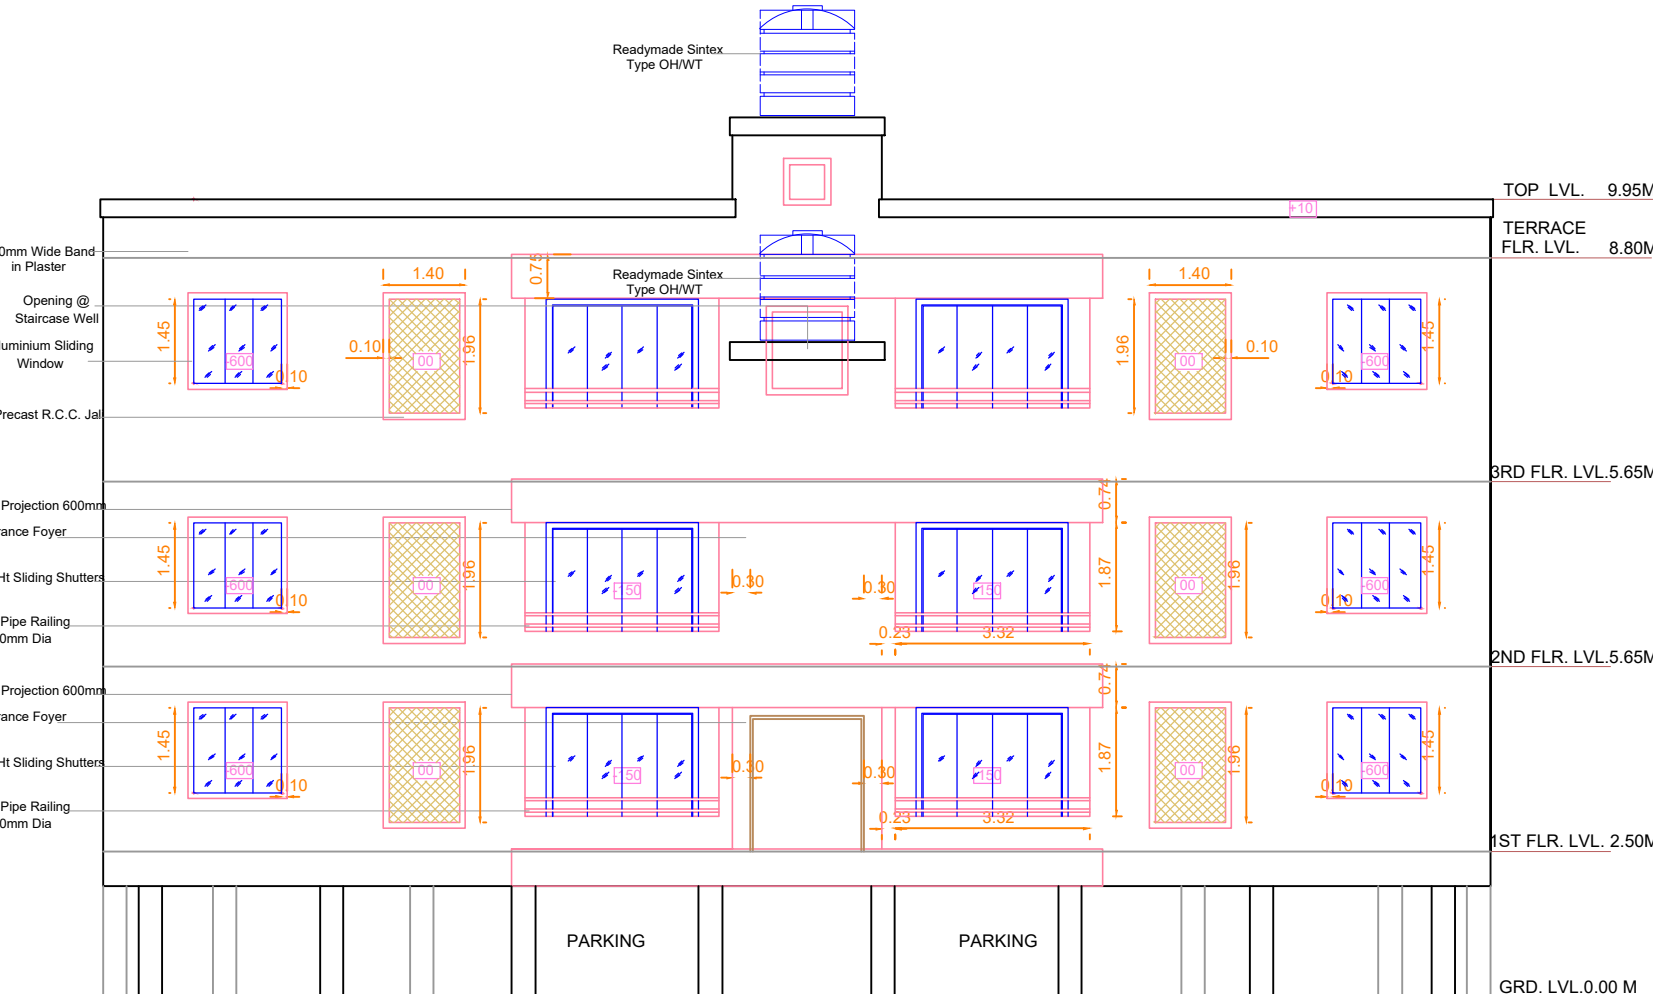


TYPICAL FRONT ELEVATION
SOUTH FACE

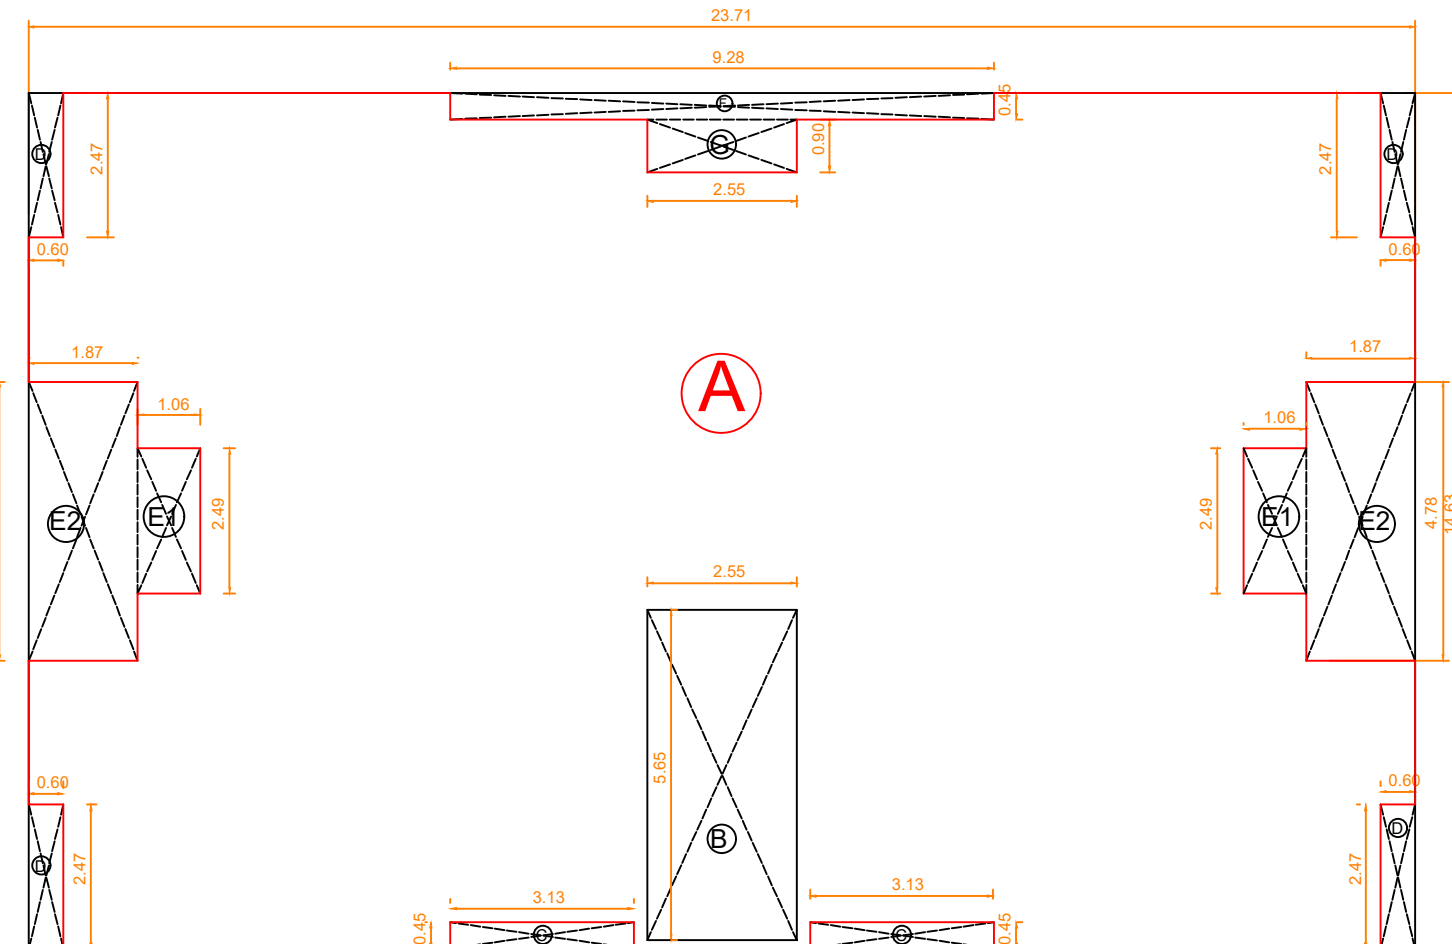


BLOCK PLAN TYPICAL G+2


SCALE:1:100

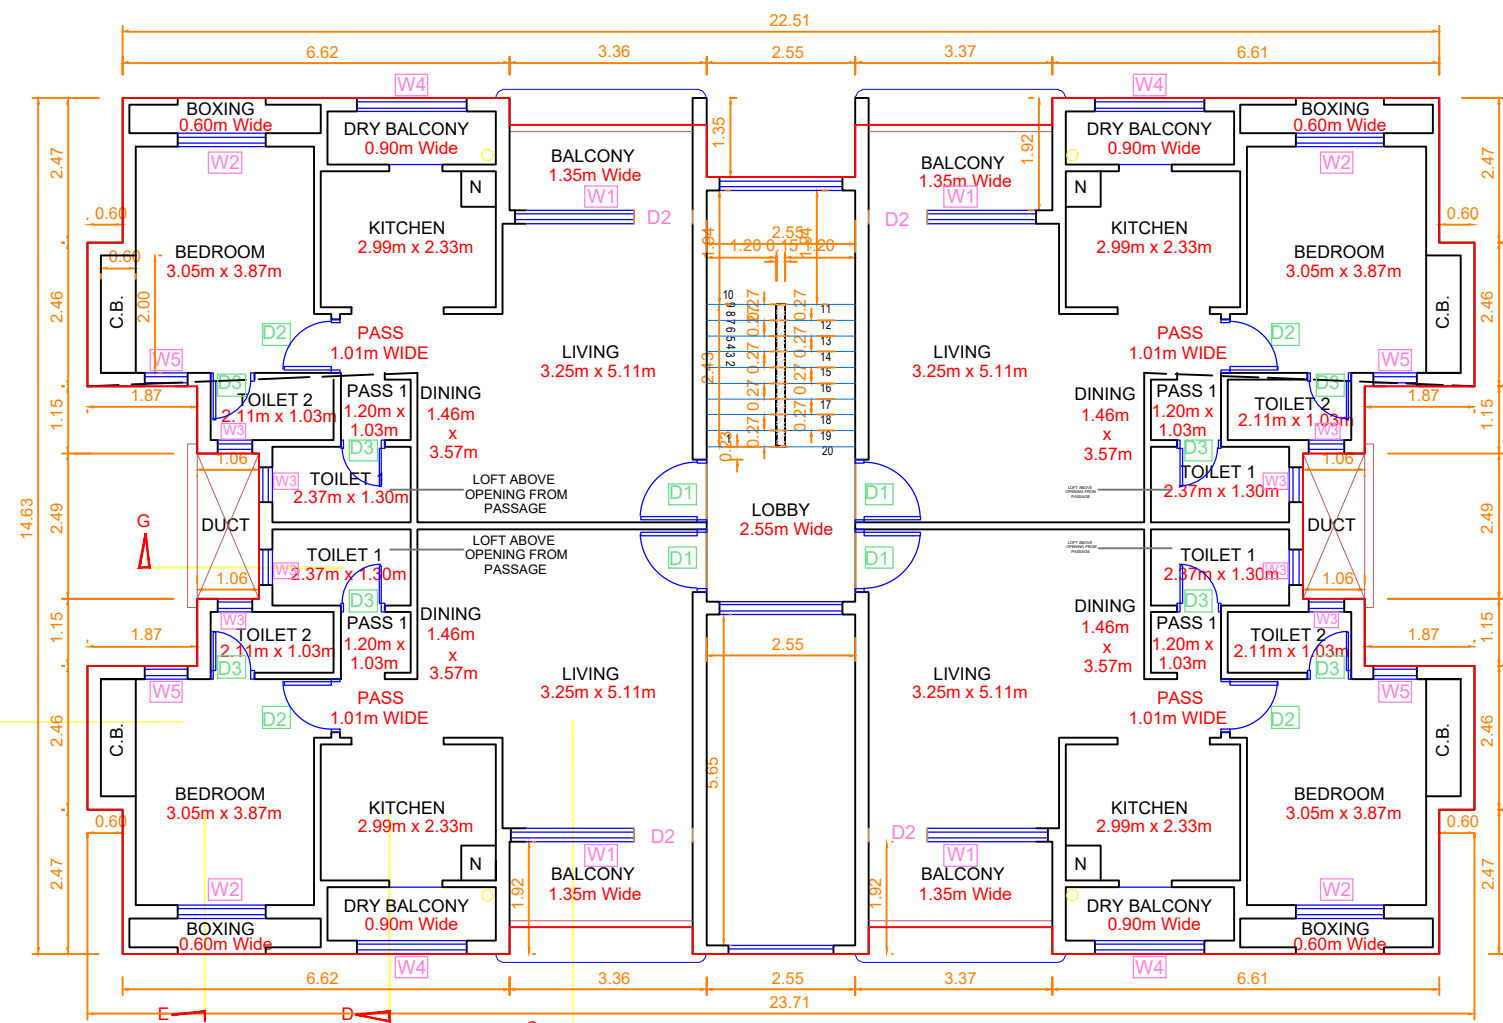

PROPOSED 1ST FLOOR PLAN

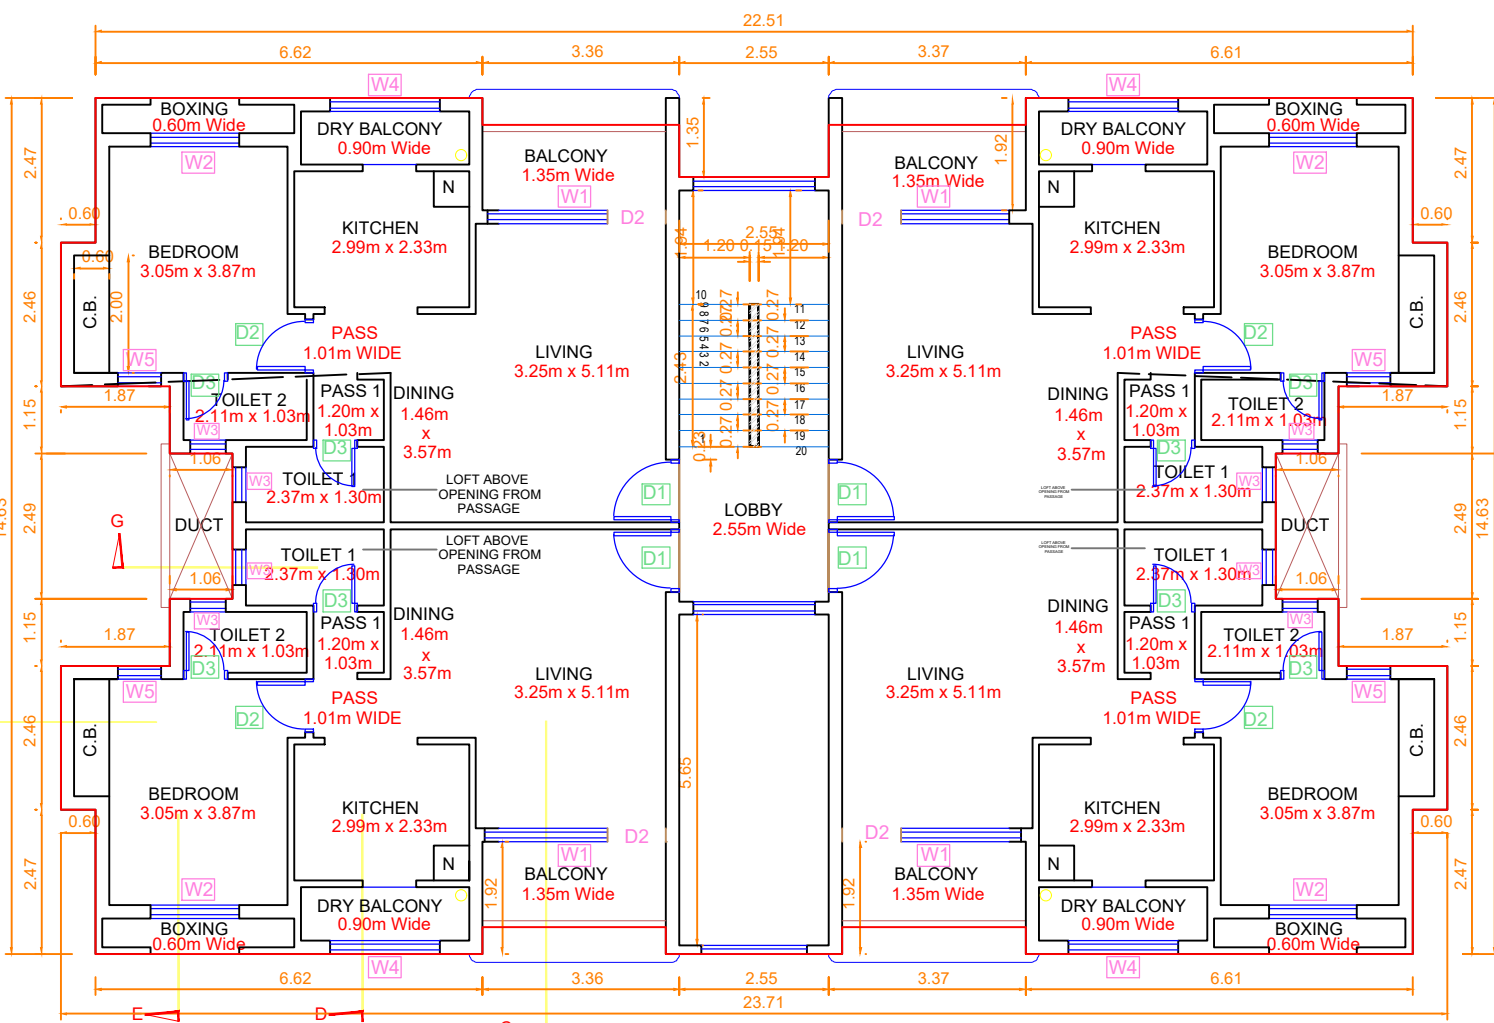

PROPOSED 2ND FLOOR PLAN

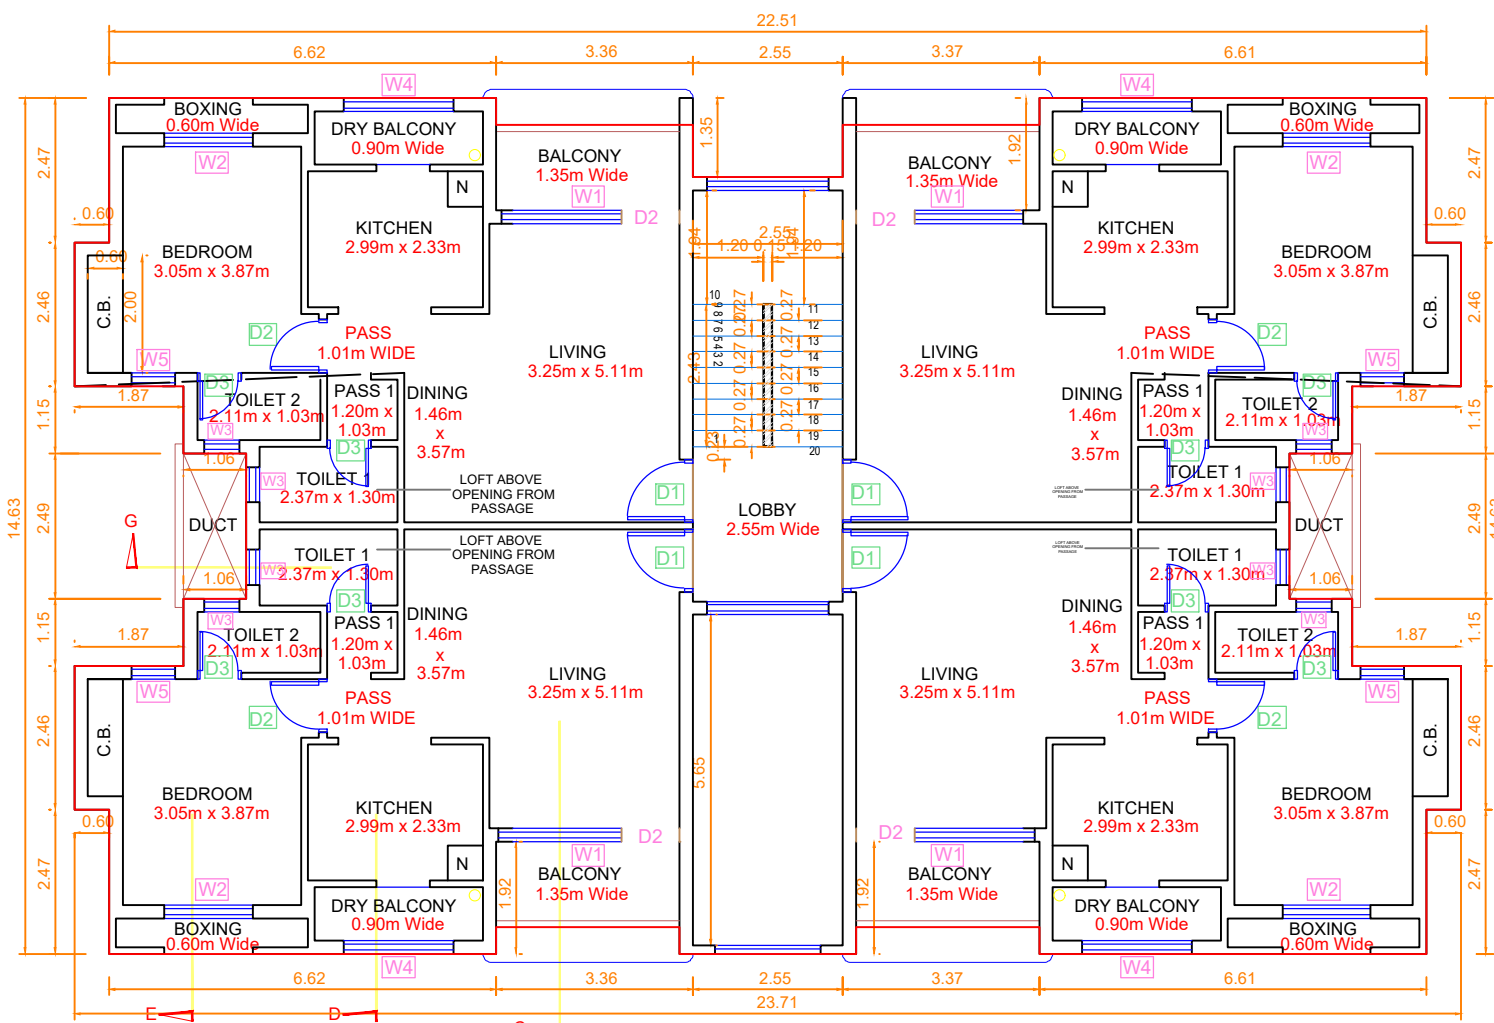

PROPOSED 3RD FLOOR PLAN

AREA CALCULATION

PROPOSED FIRST FL. BUILT UP AREA
A = 23.71 X 14.63 = 346.88 Sqm
DEDUCTION
B = 2.55 X 5.65 = 14.40 Sqm
C = 3.13 X 0.45 X 2 = 2.08 Sqm
D = 0.60 X 2.47 X 4 = 5.93 Sqm
E1 = 1.06 X 2.48 X 2 = 2.64 Sqm
E2 = 1.87 X 4.78 X 2 = 8.94 Sqm
F = 9.28 X 0.45 = 4.18 Sqm
G = 2.55 X 0.90 = 2.29 Sqm
TOTAL DEDUCTION = 47.46 Sqm
(A-TOTAL DEDUCTION) = 346.88 - 47.46 = 306.42 Sqm
[TOTAL F.FLR BUILT UP AREA = 306.42 Sqm]
[TOTAL S.FLR BUILT UP AREA = 306.42 Sqm]
[TOTAL S.FLR BUILT UP AREA = 306.42 Sqm]
[FSI FREE STILT FLR/PARKING AREA = 306.42 Sqm]

WINDOWS SCHEDULE

S.No.	DESIGNATION	Size	No	REMARKS
1	W1 (Main Window)	3400mmx2390mm	12	ALUMINUM OPENABLE WINDOW WITH MS GRILL
2	W2 (BED ROOM)	1500mmx1450mm	12	ALUMINUM OPENABLE WINDOW WITH MS GRILL
3	W3 (Toilet)	600mmx900mm	18	ALUMINUM OPENABLE WINDOW WITH MS GRILL
4	W4 (Kt)	1200mmx1960mm	12	ALUMINUM OPENABLE WINDOW WITH MS GRILL
5	W5 (B.R.)	740mmx1450mm	12	LOWARDED ALUMINUM OPENABLE WINDOW WITH MS GRILL

DOOR SCHEDULE

S.No.	ROOM NAME	Frame	Size	DOOR SHUTTER	No
1	D1 (Main Door)	Teak Wood of 100x75mm. size	1070mmx2100mm	SUPER QUALITY FLUSH DOOR WITH 30MM THICK SHUTTER	12
2	D2 (BED ROOM)	Teak Wood of 100x75mm. size	910mmx2100mm	SUPER QUALITY FLUSH DOOR WITH 30MM THICK SHUTTER	12
3	D3 (BED ROOM)	PRECAST REINFORCED CEMENT CONCRETE FRAME	790mmx1950mm	ECO BOARD OF ONE SIDE LAMINATED	24

NAME OF WORK:-

CONSTRUCTION OF CLASS-III RESIDENTIAL QUARTERS AT NAGOTHANE COLONY

MIDC

ENGINEERING
DEPARTMENT

OFFICE OF THE EXECUTIVE ENGINEER, ALIBAUG.

NAGOTHANE INDUSTRIAL AREA...

NAME OF WORK - CONST. OF CLASS III QUARTER

BY. ENGINEER.	EX. ENGINEER.	SUPTG. ENGINEER.	CHIEF. ENGINEER.
DRN.	DATE 05/04/2018	DE / STR-2/KH/	/ 18
TRD.	SCALE		